Drawings Prepared For:

Berkley

Window Schedule					
Mark	Count	Size	Description	Header Size	Window Area
W01	2	6' - 0" x 5' - 6"0	TWIN S.H. WINDOW	(2) 2x12	67 SF
W02	3	3' - 0" x 5' - 6"0	S.H. WINDOW	(2) 2x10	51 SF
W03	1	3' - 0" x 3' - 0"0	S.H. WINDOW	(2) 2x10	9 SF
					127 SF

SQFT Schedule	
Area	Name
1560 SF	LIVING SPACE
420 SF	GARAGE
416 SF	FRONT PORCH

Cabinetry Length
Overall Length
38' - 3"

Door Schedule					
Mark	Count	Size	Description	Header Size	Door Area
D01	1	3' - 0" x 6' - 8"	EXT. DOOR W/ SIDELIGHTS	(2) 2X12	38 SF
D02	1	6' - 0" x 6' - 8"	EXT. DOOR 3/4 GLASS	(2) 2X12	42 SF
D03	1	3' - 0" x 6' - 8"	EXT. DOOR 1/2 GLASS	(2) 2X10	21 SF
D04	1	3' - 0" x 6' - 8"	EXT. DOOR W/ SELF CLOSING HINGES	(2) 2X10	0 SF
D05	7	2' - 8" x 6' - 8"	INT. DOOR	(2) 2X6	0 SF
D06	1	1' - 8" x 6' - 8"	INT. DOOR	(2) 2X6	0 SF
D07	2	5' - 0" x 6' - 8"	INT. DBL. DOOR	(2) 2X6	0 SF
D08	1	4' - 0" x 6' - 8"	WALL OPENING	(2) 2X6	0 SF
D09	1	10' - 0" x 7' - 0"	GARAGE DOOR	(2) 11 7/8" LVLs	70 SF
					171 SF

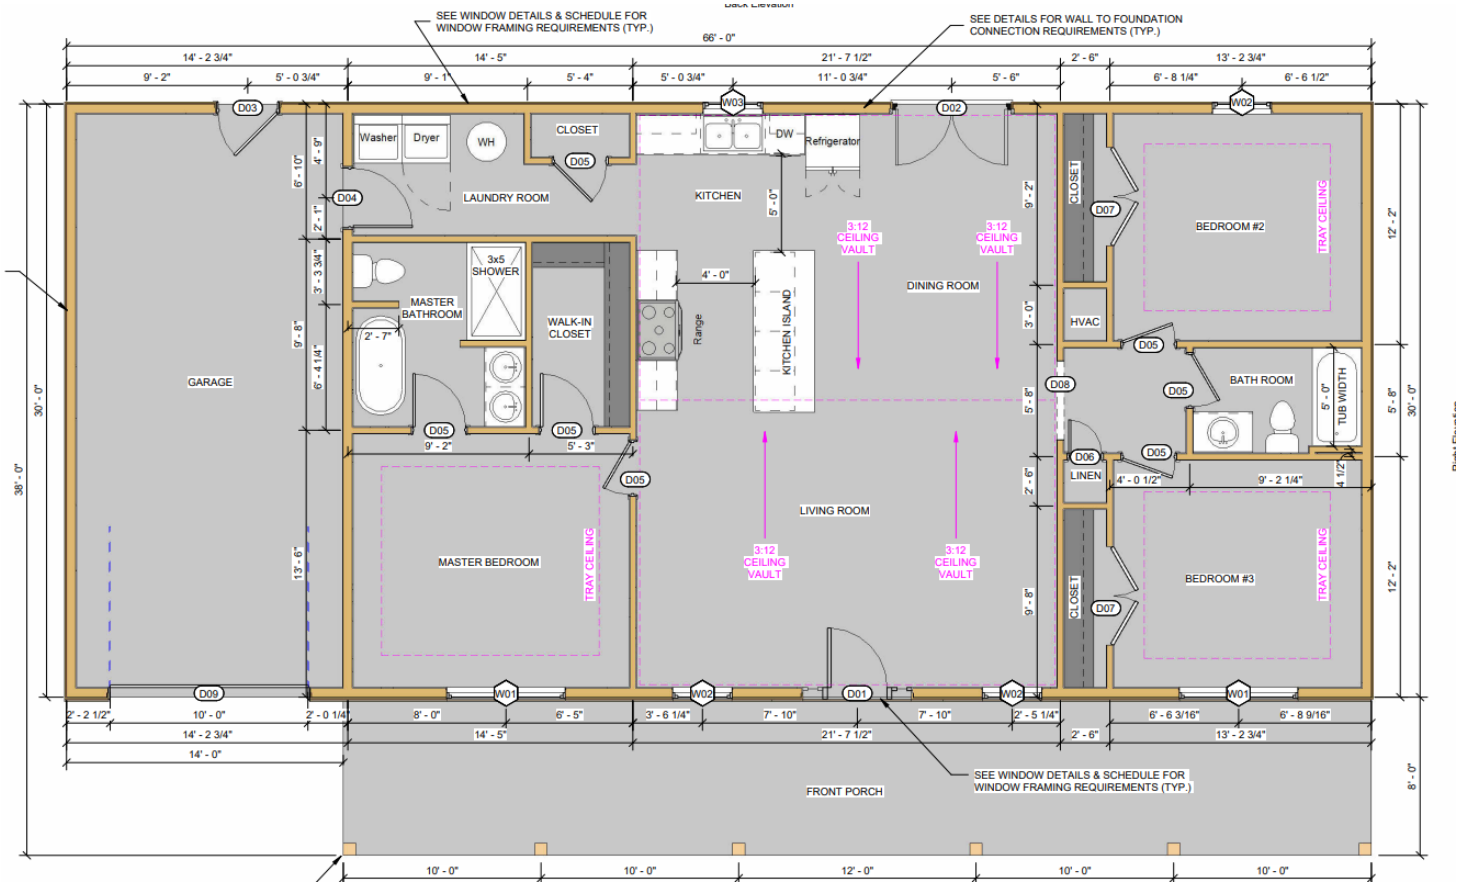

BERKLEY CABINET DESIGNS

KITCHEN

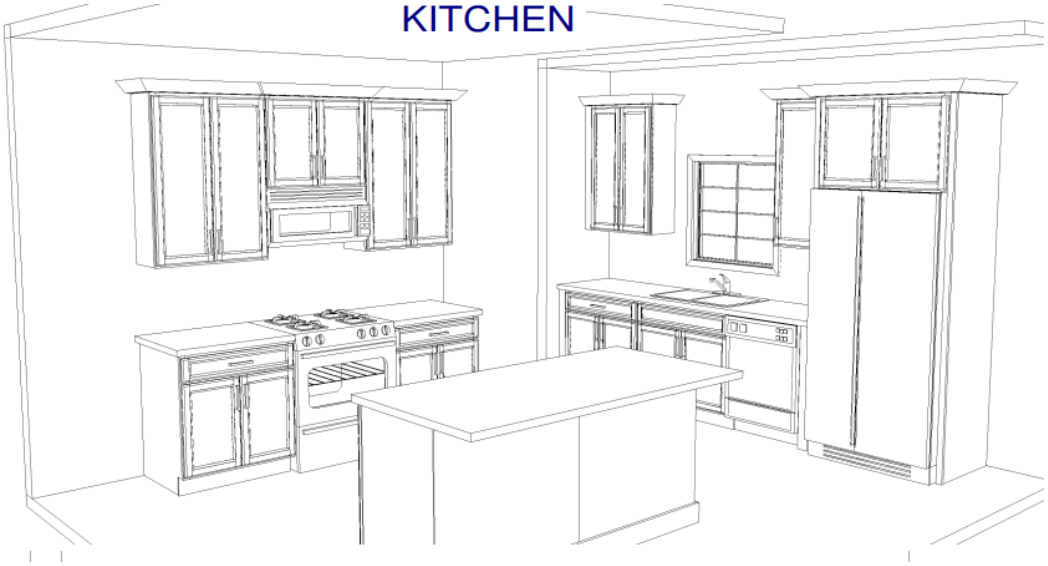

ISLAND

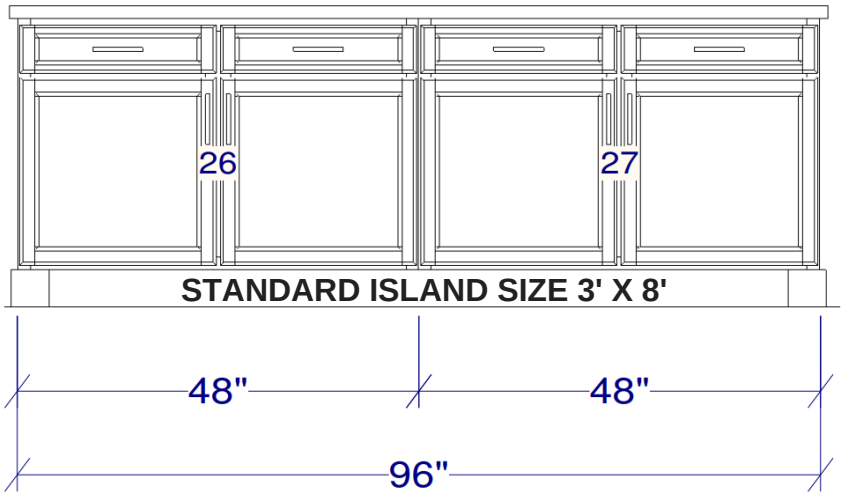

MASTER BATH

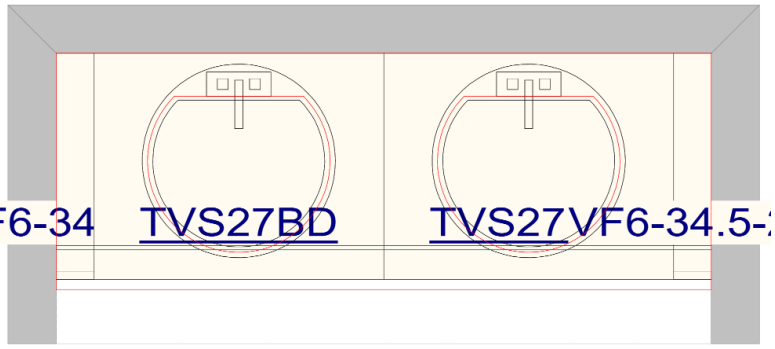

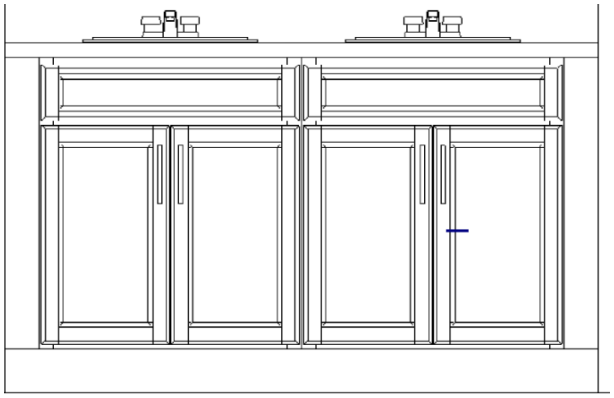
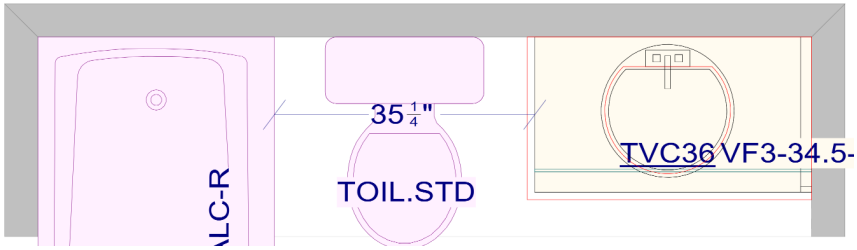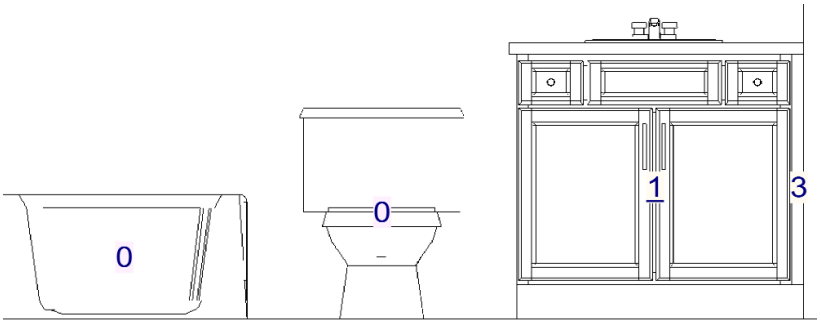
BATH 2