Drawings Prepared For:

Daughtery Barndominium

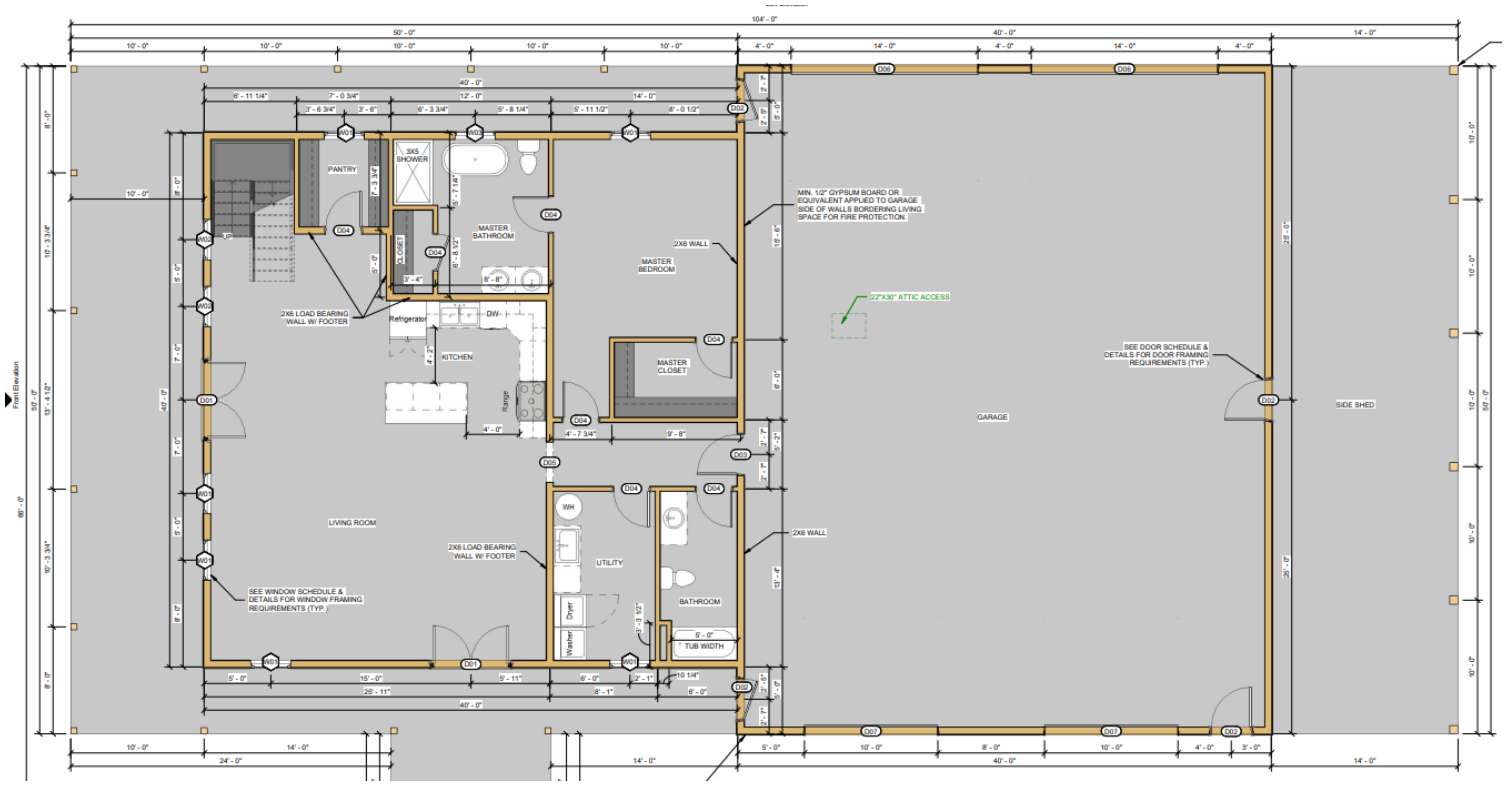

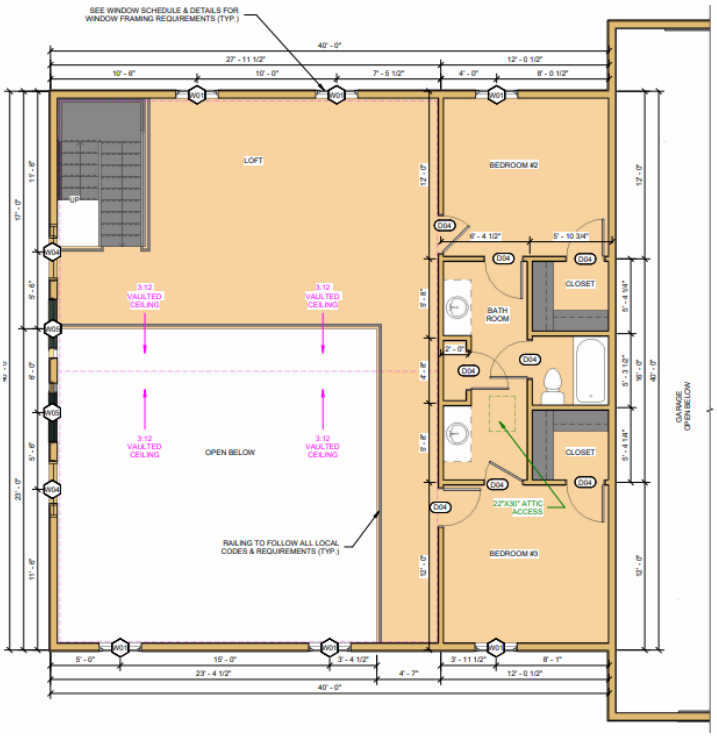

SQFT Schedule	
Area	Name
2000 SF	GARAGE SLAB
1600 SF	HOUSE SLAB
1092 SF	PORCH SLAB
1005 SF	2ND FLOOR
700 SF	SIDE SHED SLAB

Cabinetry Length
Width
58' - 6"

Window Schedule

Mark	Count	Size	Description	Header Size	Window Area
W01	12	3' - 0" x 5' - 6"0	S.H. WINDOW	(2) 2X10	202 SF
W02	2	3' - 0" x 5' - 6"0	S.H. WINDOW **TEMP**	(2) 2X10	34 SF
W03	1	3' - 0" x 4' - 0"0	FIXED WINDOW **TEMP**	(2) 2X10	12 SF
W04	2	4' - 0" x 5' - 8"0	FIXED TRAPIZOIDAL WINDOW	PER MANUF.	39 SF
W05	2	4' - 0" x 4' - 0"0	FIXED RHOMBUS WINDOW	PER MANUF.	41 SF
					328 SF

Door Schedule1

Mark	Count	Size	Description	Header Size	Door Area
D01	2	6' - 0" x 6' - 8"	EXT. FRENCH DOOR 3/4 GLASS	(2) 2X12	83 SF
D02	4	3' - 0" x 6' - 8"	EXT. DOOR 1/2 GLASS	(2) 2X10	86 SF
D03	1	3' - 0" x 6' - 8"	EXT. DOOR W/ SELF CLOSING HINGES	(2) 2X10	0 SF
D04	15	2' - 8" x 6' - 8"	INT. DOOR	(2) 2X6	0 SF
D05	1	3' - 0" x 6' - 8"	WALL OPENING	(2) 2X10	0 SF
D06	2	14' - 0" x 12' - 0"	GARAGE DOOR	(2) 14" LVLs	336 SF
D07	2	10' - 0" x 12' - 0"	GARAGE DOOR	(2) 11 7/8" LVLs	240 SF
					745 SF

DAUGHTERY CABINET DESIGNS

KITCHEN

UPGRADED ISLAND SIZE SHOWN

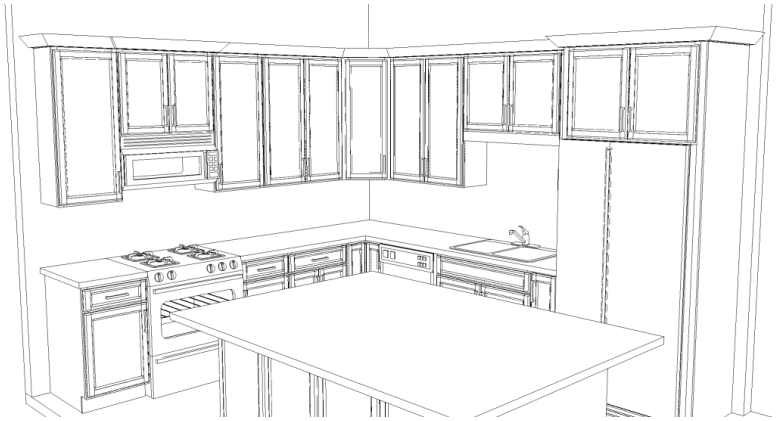

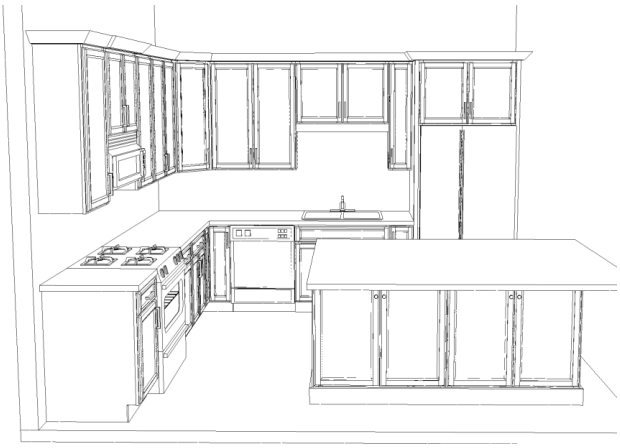

ISLAND

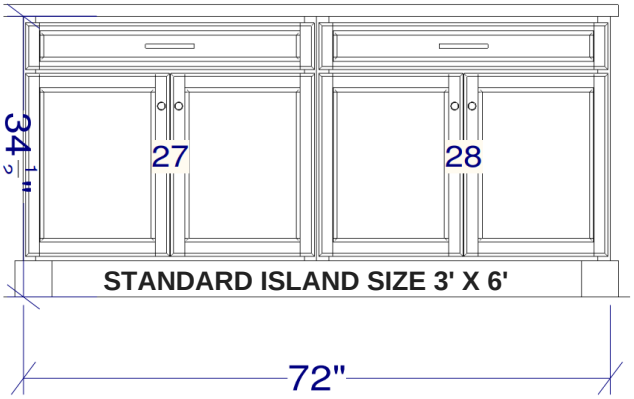

LAUNDRY

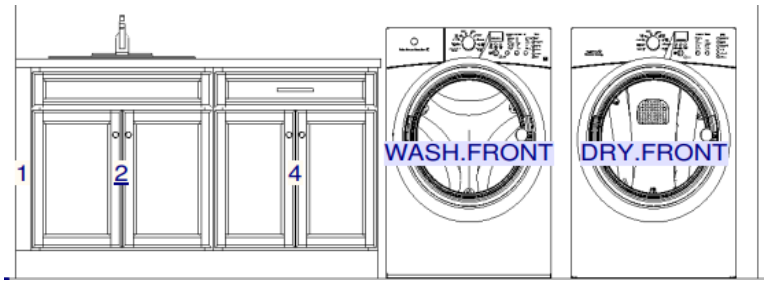

MASTER BATH

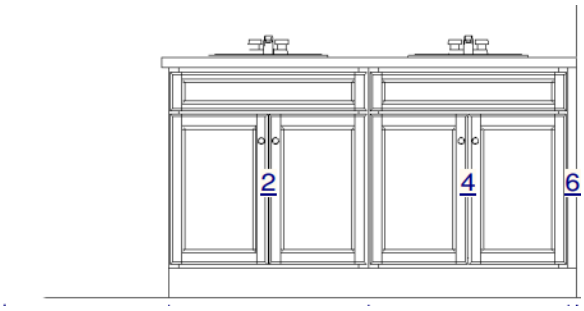

HALF BATH

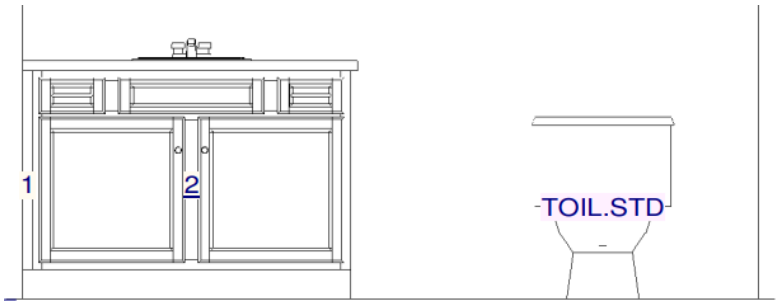
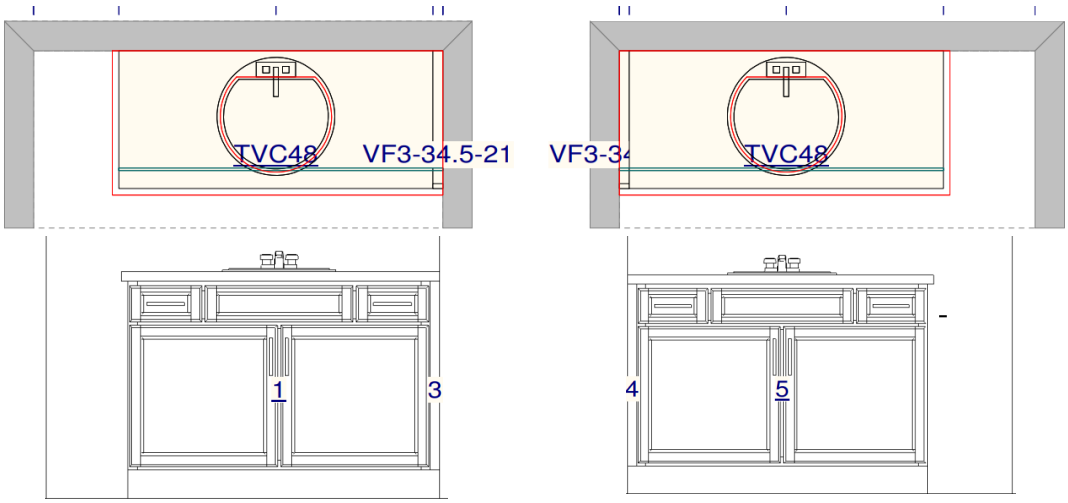
JACK AND JILL BATH