Drawings Prepared For:

Huntley Home

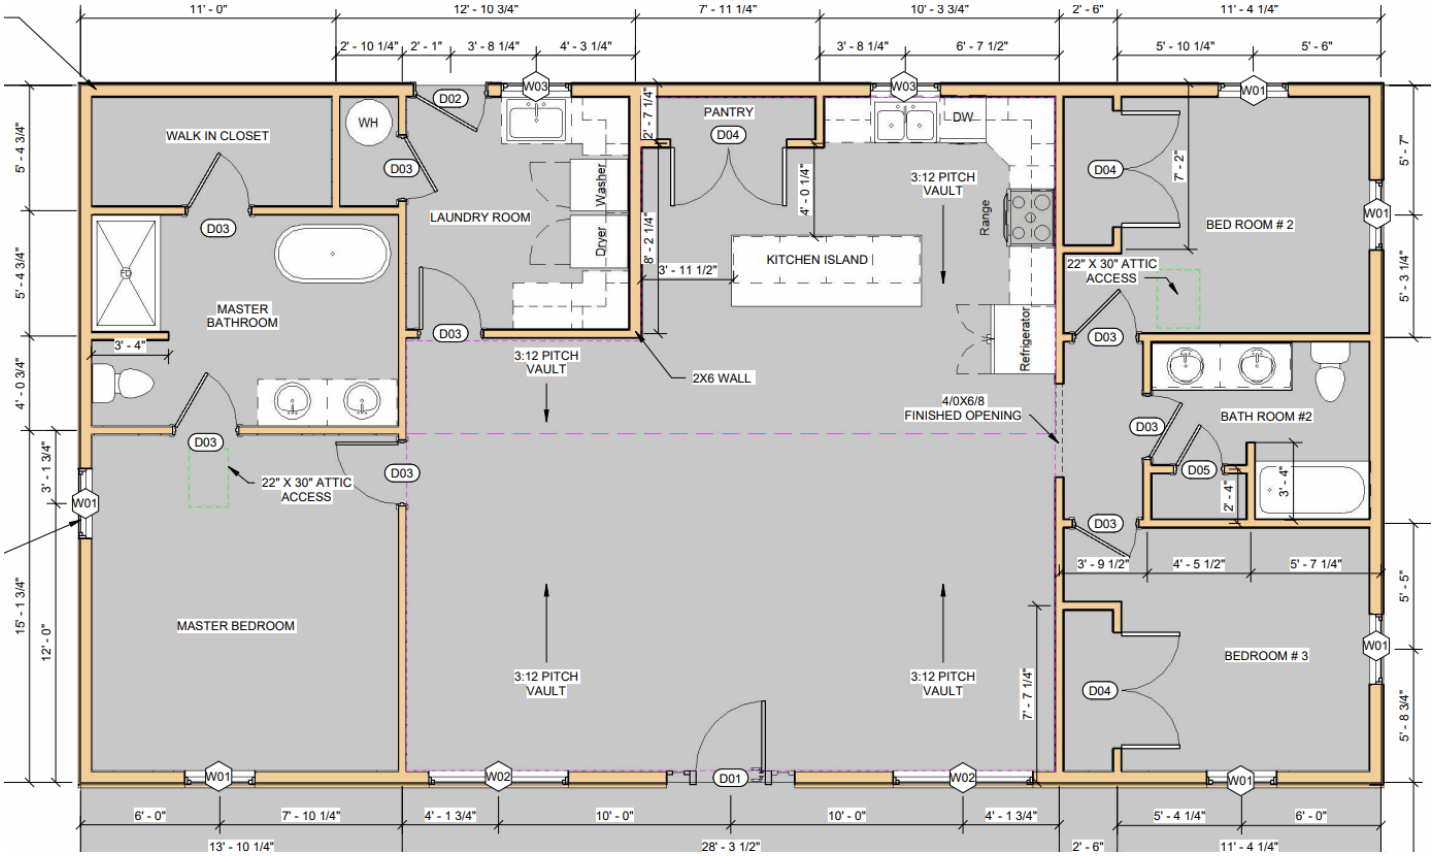

Cabinetry Length
Width
68' - 9"

SQFT Schedule1	
Area	Name
1680 SF	Living Area
448 SF	Front Porch

Door Schedule

Mark	Count	Size	Description	Header Size	Door Area
D01	1	3' - 0" x 6' - 8"	Ext. 1/2 GlassR.H. W/ (2) 12" Side Lites	(2) 2x12	42 SF
D02	1	3' - 0" x 6' - 8"	Ext. 1/2 Glass R.H.	(2) 2x10	21 SF
D03	8	2' - 8" x 6' - 8"	Interior Door	(2) 2x6	0 SF
D04	3	5' - 0" x 6' - 8"	Interior Swing	(2) 2x6	0 SF
D05	1	2' - 0" x 6' - 8"	Interior Door	(2) 2x6	0 SF
					63 SF

Window Schedule

Mark	Count	Size	Description	Header Size	Window Area
W01	6	3' - 0" x 5' - 6"0	Single Hung	(2) 2x10	101 SF
W02	2	6' - 0" x 5' - 6"0	3 x 5 Twin Single Hung	(2) 2x12	67 SF
W03	2	3' - 0" x 3' - 0"0	<varies>	(2) 2x10	19 SF
					187 SF

HUNTLEY CABINET DESIGNS

KITCHEN

ISLAND

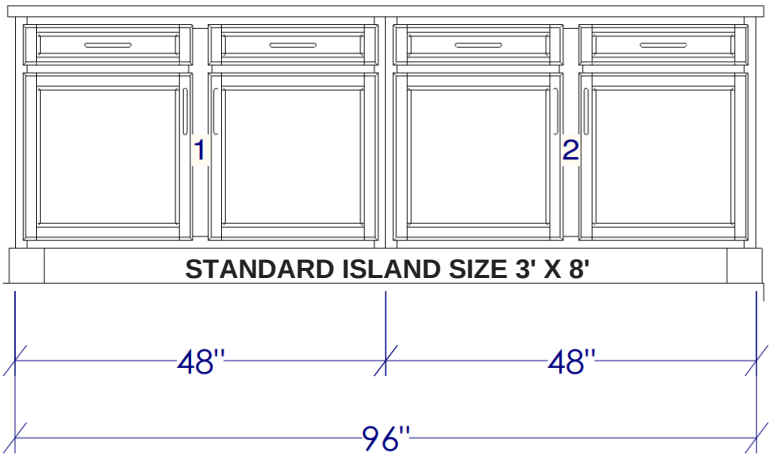

LAUNDRY

MASTER BATH

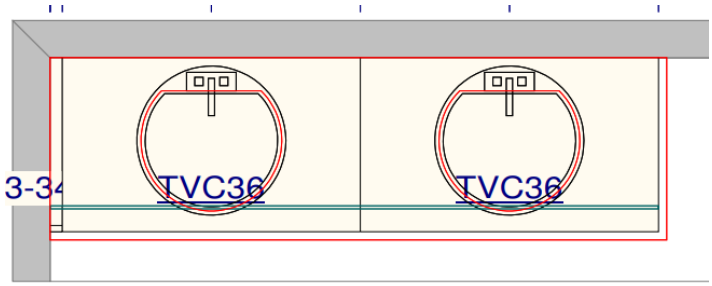

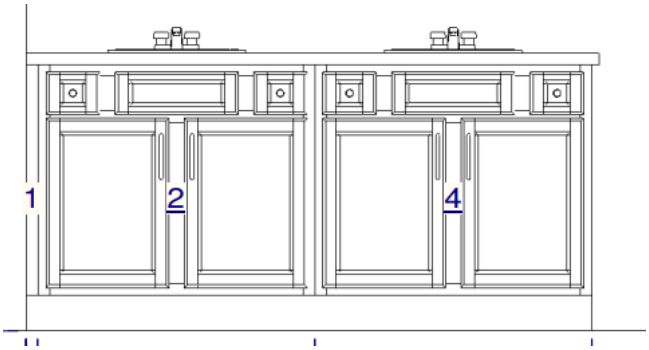
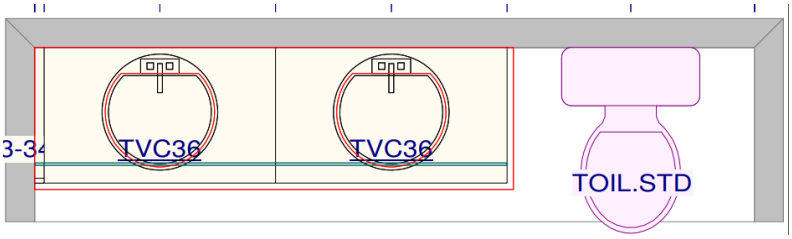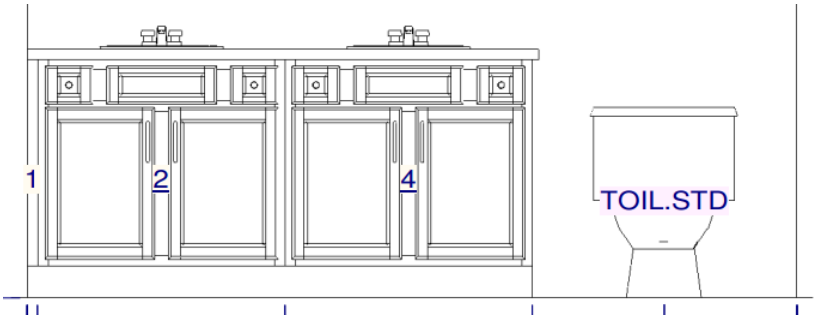
BATH 2