Drawings Prepared For:

Huntley 2.0

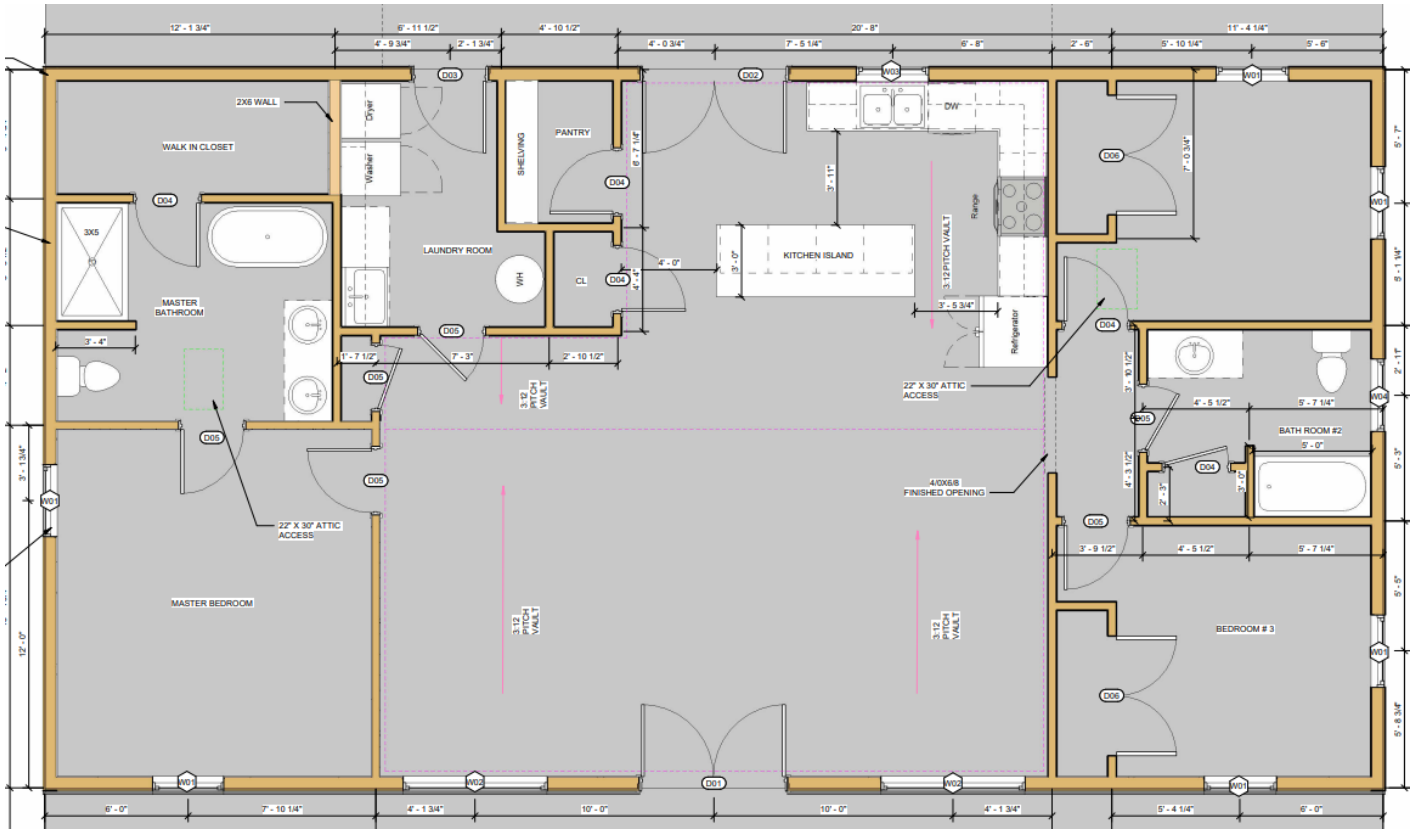

Cabinetry Length
Width
57' - 9"

SQFT Schedule	
Area	Name
1680 SF	Living Area
448 SF	Front Porch
448 SF	Back Porch

Door Schedule

Mark	Count	Size	Description	Header Size	Door Area
D01	1	6' - 0" x 6' - 8"	EXT. FRENCH 3/4 GLASS	(2) 2x10	42 SF
D02	1	6' - 0" x 6' - 8"	EXT. FRENCH DOOR FULL GLASS	(2) 2X10	42 SF
D03	1	3' - 0" x 6' - 8"	EXTERIOR L.H. 1/2 GLASS	(2) 2X10	21 SF
D04	5	2' - 8" x 6' - 8"	INTERIOR R.H.	(2) 2x6	0 SF
D05	6	2' - 8" x 6' - 8"	INTERIOR L.H.	(2) 2x6	0 SF
D06	2	5' - 0" x 6' - 8"	INTERIOR DOUBLE DOOR	(2) 2x6	0 SF
					105 SF

Window Schedule

Mark	Count	Size	Description	Header Size	Window Area
W01	6	3' - 0" x 5' - 6"0	SINGLE HUNG	(2) 2x10	101 SF
W02	2	6' - 0" x 5' - 6"0	SINGLE HUNG TWIN	(2) 2x10	67 SF
W03	1	3' - 0" x 3' - 0"0	SINGLE HUNG	(2) 2x10	9 SF
W04	1	3' - 0" x 3' - 0"0	SINGLE HUNG **TEMPERED**	(2) 2x10	9 SF
					187 SF

HUNTLEY 2.0 CABINET DESIGNS

KITCHEN

ISLAND

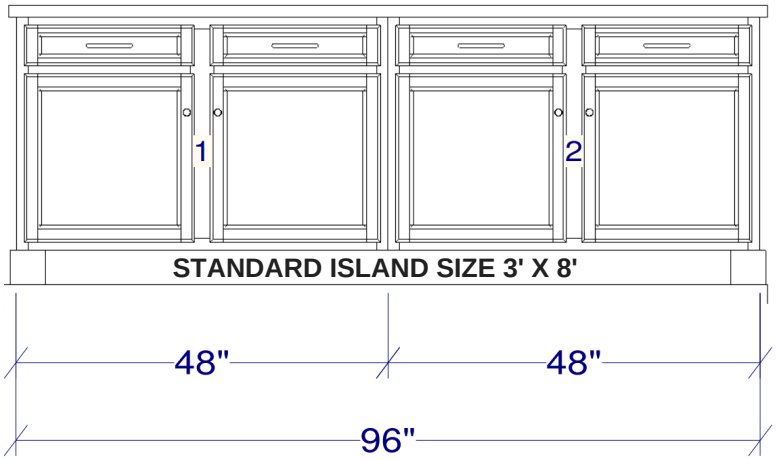

LAUNDRY

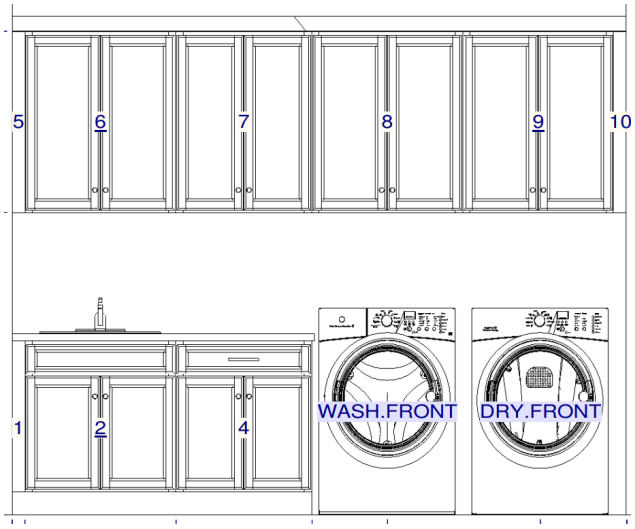

MASTER BATH

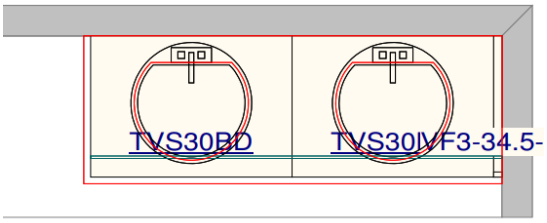

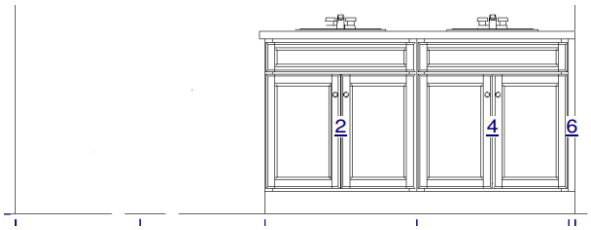
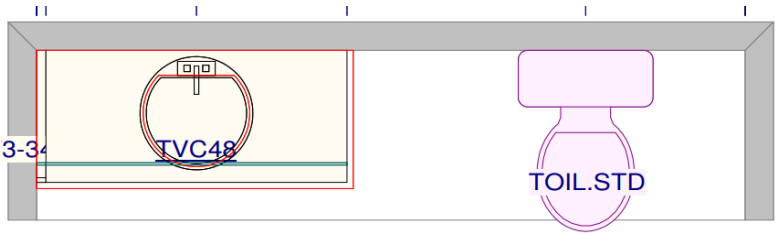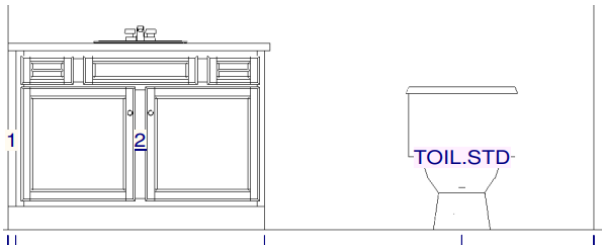
BATH 2