Drawings Prepared For:

Martin Lodge

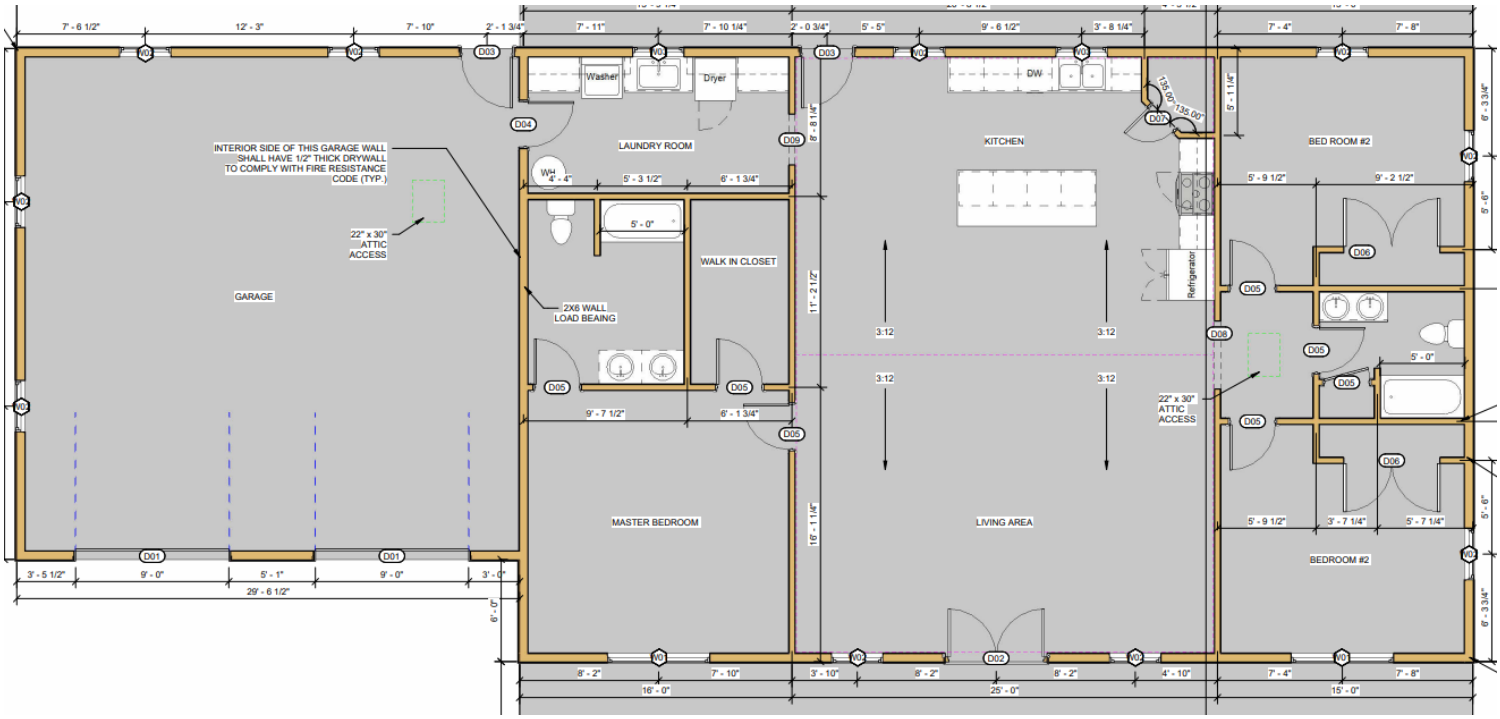

Cabinetry Length
Width
74' - 0"

Window Schedule

Mark	Count	Size	Description	Header Size	Window Area
W01	2	6' - 0" x 5' - 6"0	3/0X5/6 Twin Single Hung	(2) 2x10	67 SF
W02	10	3' - 0" x 5' - 6"0	Single Hung	(2) 2x10	169 SF
W03	2	3' - 0" x 3' - 0"0	Single Hung	(2) 2x10	19 SF
					254 SF

SQFT Schedule

Area	Name
2016 SF	Main Living Area
886 SF	Garage
448 SF	Front Porch
560 SF	Back Porch

Door Schedule1

Mark	Count	Size	Description	Header Size	Door Area
D01	2	9' - 0" x 8' - 0"	Garage Door	(2) 2X12	148 SF
D02	1	6' - 0" x 6' - 8"	Ext. French Door	(2) 2X12	40 SF
D03	2	3' - 0" x 6' - 8"	Ext Door	(2) 2x10	43 SF
D04	1	2' - 8" x 6' - 8"	Solid panel (Self Closing Hinges)	(2) 2x10	0 SF
D05	7	2' - 8" x 6' - 8"	Int. Door	(2) 2X6	0 SF
D06	2	5' - 8" x 6' - 8"	Int. Double Door	(2) 2X6	0 SF
D07	1	2' - 0" x 6' - 8"	Int. Door	(2) 2X6	0 SF
D08	1	4' - 0" x 6' - 8"	Int. Finished Opening	(2) 2X6	0 SF
D09	1	3' - 0" x 6' - 8"	Int. Finished Opening	(2) 2X6	0 SF
					231 SF

MARTIN LODGE CABINET DESIGNS

KITCHEN

LAUNDRY

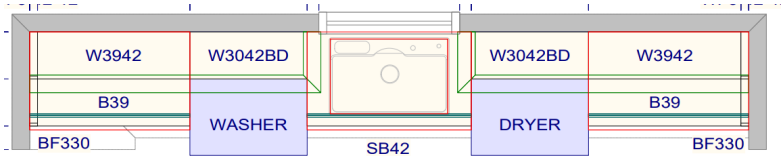

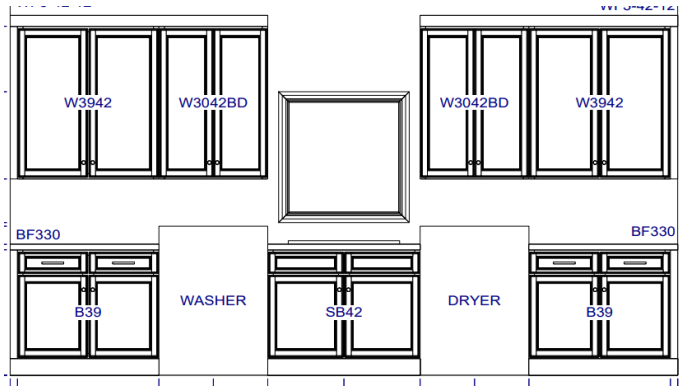

ISLAND

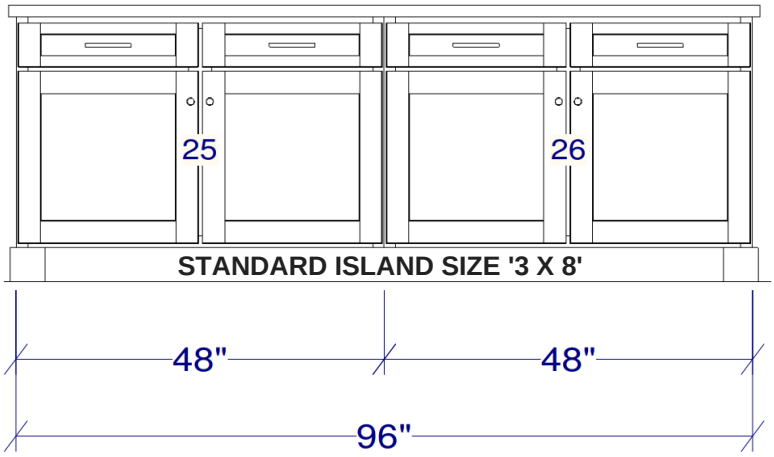

MASTER BATH

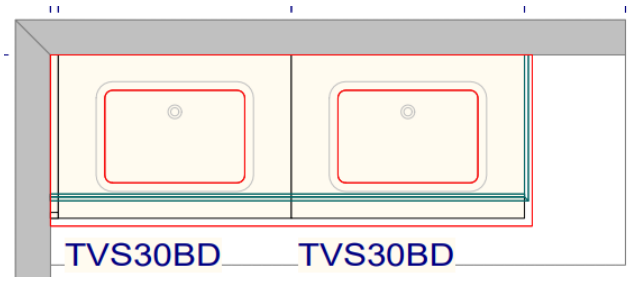

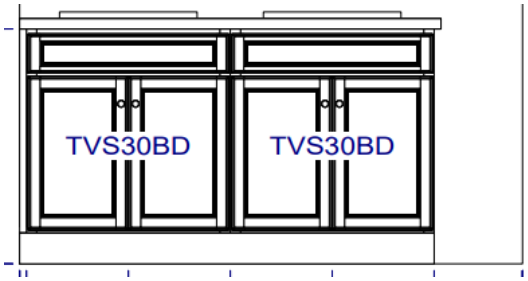
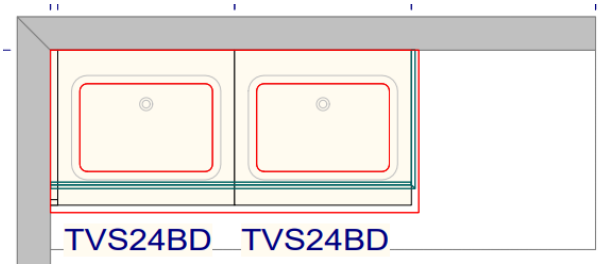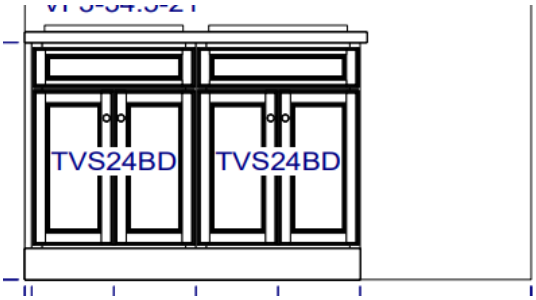
GUEST BATH