Drawings Prepared For:

Meadows End

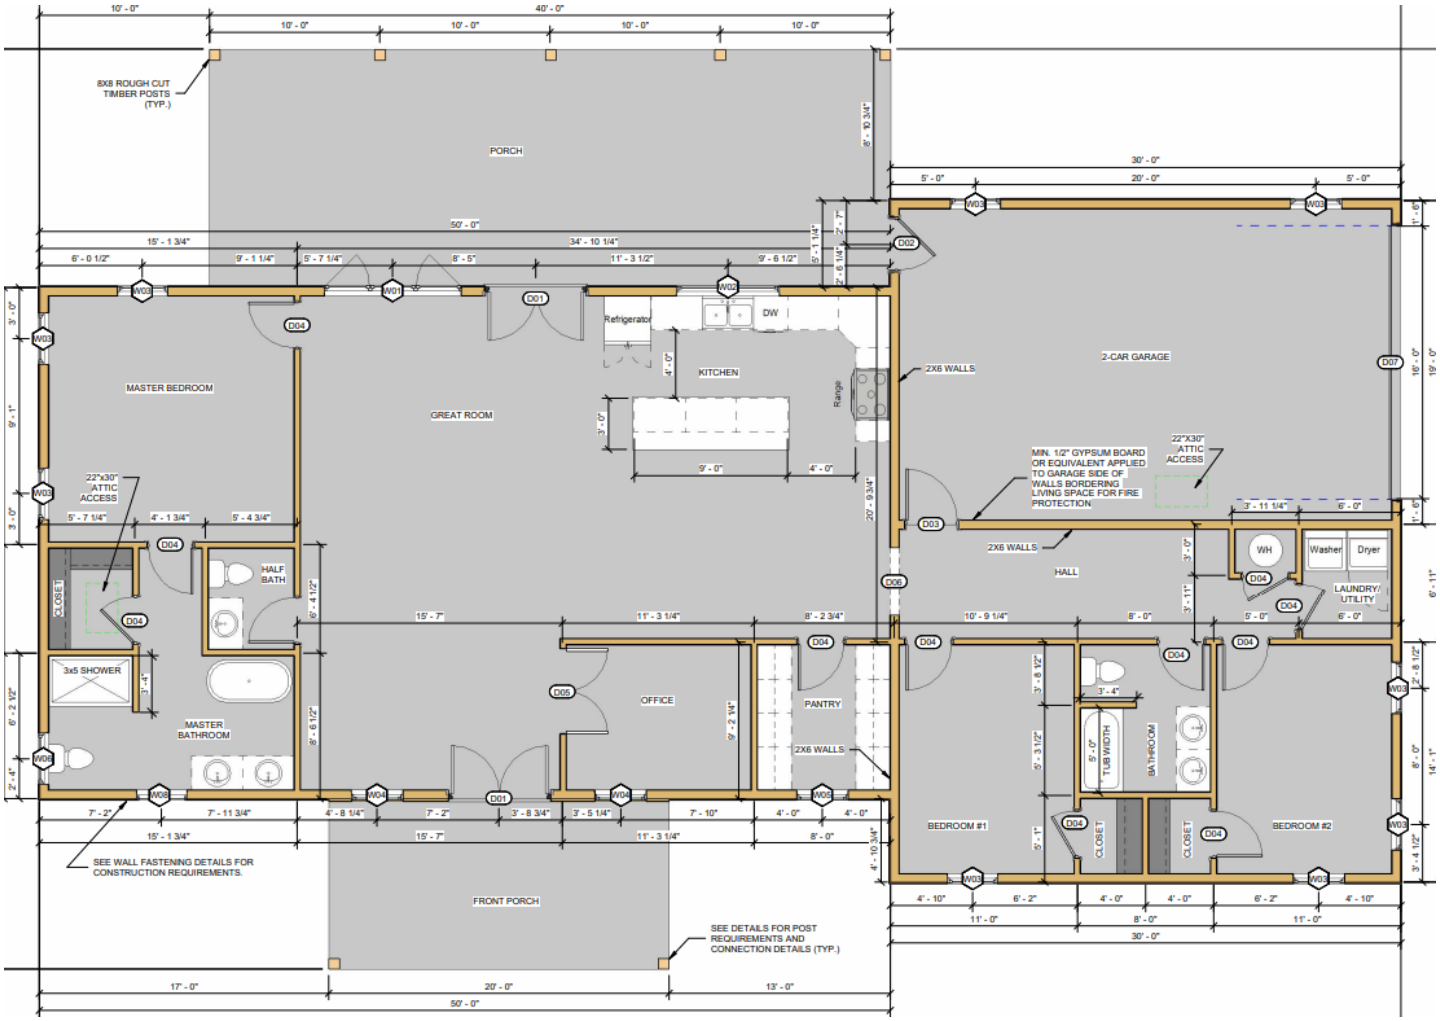

Cabinetry Length
Width
73' - 6"

Door Schedule

Mark	Count	Size	Description	Header Size	Door Area
D01	2	6' - 0" x 6' - 8"	EXT. FRENCH DOOR 3/4 GLASS	(2) 2X12	83 SF
D02	1	3' - 0" x 6' - 8"	EXT. DOOR	(2) 2X10	21 SF
D03	1	3' - 0" x 6' - 8"	EXT. DOOR W/ SELF CLOSING HINGES	(2) 2X6	0 SF
D04	12	2' - 8" x 6' - 8"	INT. DOOR	(2) 2X6	0 SF
D05	1	5' - 0" x 6' - 8"	INT. FRENCH DOOR	(2) 2X6	0 SF
D06	1	4' - 0" x 6' - 8"	WALL OPENING	(2) 2X10	0 SF
D07	1	16' - 0" x 8' - 0"	GARAGE DOOR	(2) 16" LVLs	128 SF
					233 SF

SQFT Schedule

Area	Name
2130 SF	LIVING SPACE
570 SF	GARAGE
200 SF	FRONT PORCH
560 SF	BACK PORCH

Window Schedule

Mark	Count	Size	Description	Header Size	Window Area
W01	1	8' - 0" x 6' - 0"0	TRIPLE CASEMENT WINDOW, MULLED **TEMP**	(2) 11 7/8 LVLs	49 SF
W02	1	6' - 0" x 3' - 0"0	TWIN SINGLE HUNG, MULLED	(2) 2X12	18 SF
W03	9	3' - 0" x 5' - 6"0	SINGLE HUNG WINDOW	(2) 2X10	152 SF
W04	2	3' - 0" x 5' - 6"0	SINGLE HUNG WINDOW **TEMP**	(2) 2X10	34 SF
W05	1	3' - 0" x 3' - 0"0	SINGLE HUNG WINDOW	(2) 2X10	9 SF
W06	1	3' - 0" x 3' - 0"0	SINGLE HUNG WINDOW **TEMP**	(2) 2X10	9 SF
W07	1	3' - 0" x 3' - 0"0	FIXED WINDOW	(2) 2X10	9 SF
W08	1	3' - 0" x 3' - 0"0	FIXED WINDOW **TEMP**	(2) 2X10	9 SF
					289 SF