Drawings Prepared For:

Shady Meadow

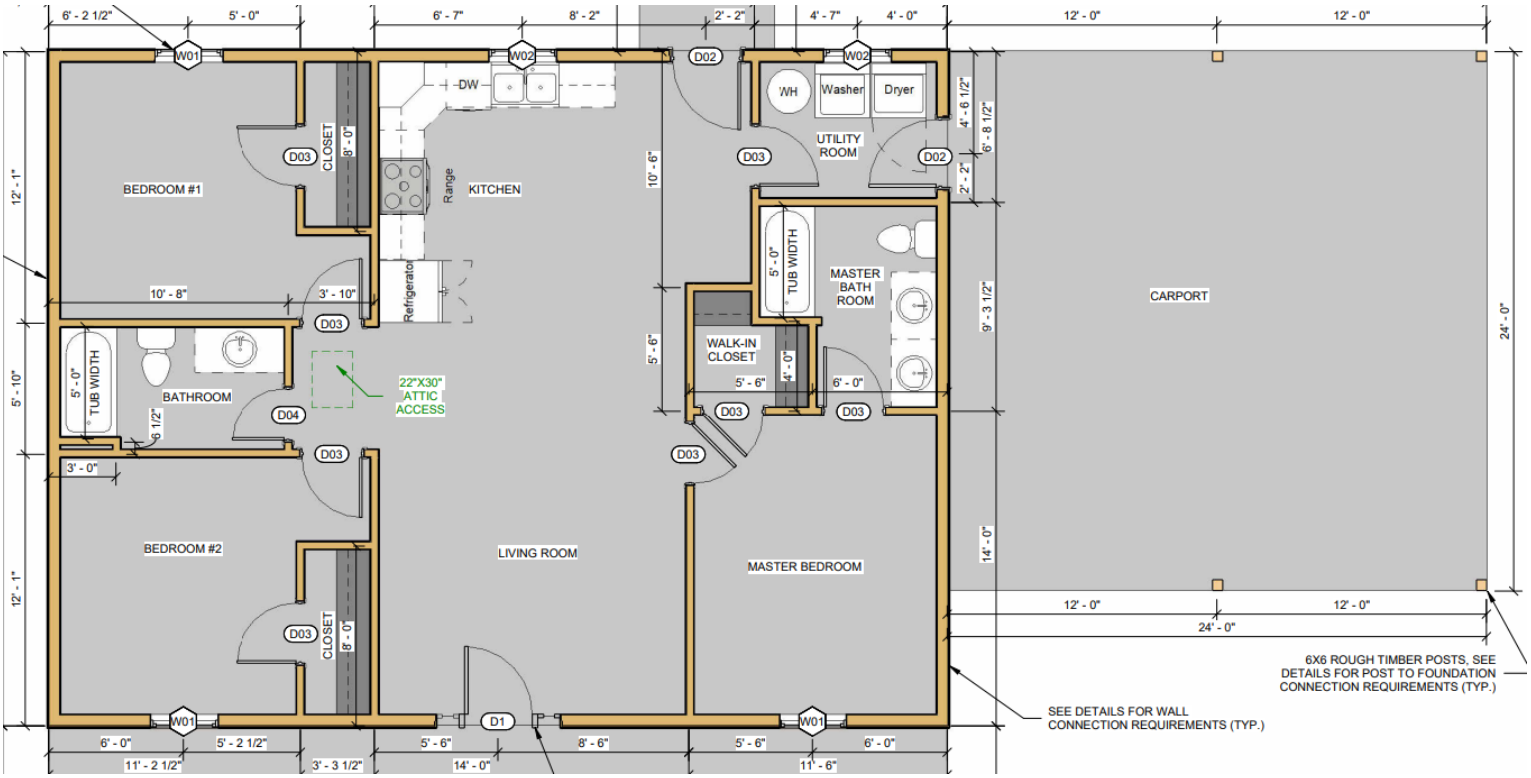

Cabinetry Length
Width
38' - 0"

Door Schedule

Mark	Count	Size	Description	Header Size	Door Area
D1	1	3' - 0" x 6' - 8"	EXT. DOOR W/ SIDELIGHTS	(2) 2X12	33 SF
D02	2	3' - 0" x 6' - 8"	EXT. DOOR 1/2 GLASS	(2) 2X10	43 SF
D03	8	2' - 8" x 6' - 8"	INT. DOOR	(2) 2X6	0 SF
D04	1	2' - 4" x 6' - 8"	INT. DOOR	(2) 2X6	0 SF
					76 SF

SQFT Schedule

Area	Name
1200 SF	HOUSE SLAB
576 SF	CARPORT SLAB
240 SF	FRONT PORCH SLAB
24 SF	BACK PORCH SLAB

Window Schedule

Mark	Count	Size	Description	Header Size	Window Area
W01	3	3' - 0" x 5' - 0"0	S.H. WINDOW	(2) 2X10	46 SF
W02	2	3' - 0" x 3' - 0"0	S.H. WINDOW	(2) 2X10	19 SF
					65 SF

SHADY MEADOW CABINET DESIGNS

KITCHEN

ISLAND NOT INCLUDED WITH STANDARD PLAN

MASTER BATH

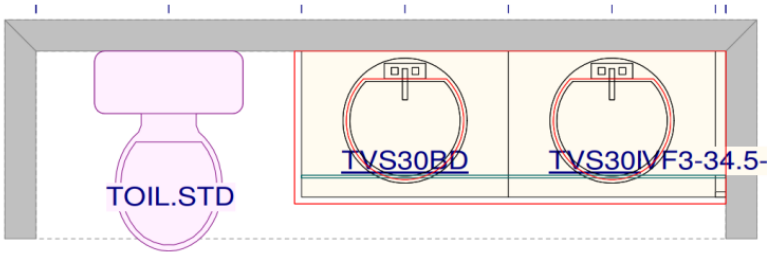

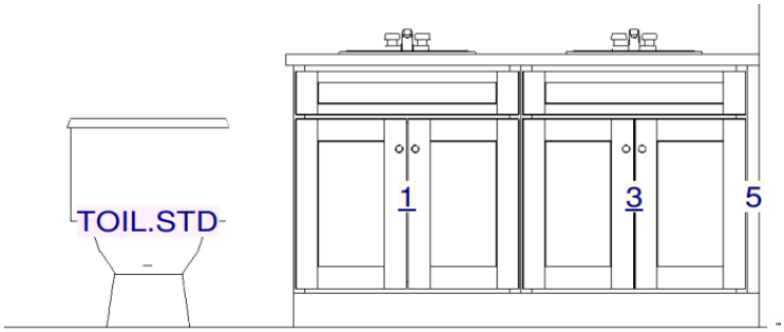
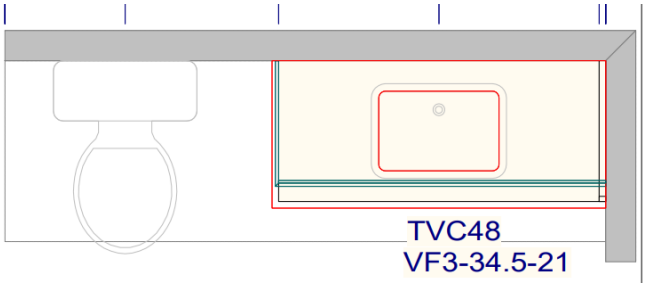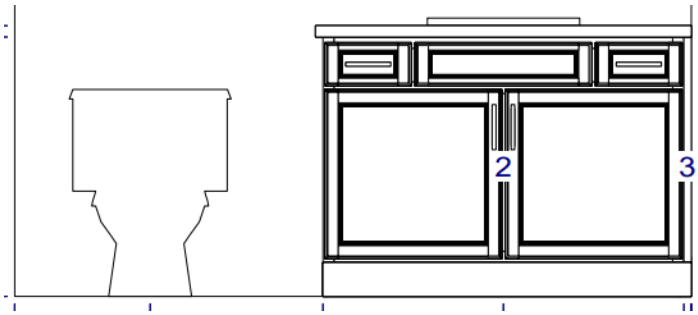
GUEST BATH